


| WINDOW SCHEDULE    |       |        |          |              |            |          |                                                                      |                                                       |  |
|--------------------|-------|--------|----------|--------------|------------|----------|----------------------------------------------------------------------|-------------------------------------------------------|--|
| WINDOW DESCRIPTION | WIDTH | HEIGHT | MATERIAL | FINISH       | # OF LITES | QUANTITY | LOCATION                                                             | REMARKS                                               |  |
| 20310 CSMT         | 2'-0" | 3'-10" | METAL    | PRE-FINISHED | 6 LITE     | 3        | OFFICE, POWDER ROOM                                                  | CASEMENT WINDOW                                       |  |
| 2446 CSMT          | 2'-4" | 4'-6"  | METAL    | PRE-FINISHED | 6 LITE     | 1        | BATH (BASEMENT)                                                      | CASEMENT WINDOW                                       |  |
| 1W 2846 CSMT       | 2'-8" | 4'-8"  | METAL    | PRE-FINISHED | 6 LITE     | 1        | JR. MASTER BATH                                                      | TWIN CASEMENT WINDOWS, TEMPERED                       |  |
| (3) 2846 CSMT      | 2'-8" | 4'-8"  | METAL    | PRE-FINISHED | 6 LITE     | 1        | SCULLERY                                                             | TRIPLE CASEMENT WINDOWS                               |  |
| 2852 FIXED         | 2'-8" | 5'-2"  | METAL    | PRE-FINISHED | 6 LITE     | 10       | DRESSING ROOM, GARAGE A, GARAGE B                                    | FIXED WINDOW                                          |  |
| 2852 CSMT          | 2'-8" | 5'-2"  | METAL    | PRE-FINISHED | 6 LITE     | 6        | GUEST SUITE, BEDROOM 5, BEDROOM 6, BATH 6                            | CASEMENT WINDOW                                       |  |
| 1W 2852 FIXED      | 2'-8" | 5'-2"  | METAL    | PRE-FINISHED | 6 LITE     | 4        | MASTER DRESSING ROOM, MASTER BATH, DRESSING ROOM NO. 6, STAIR (NEAR) | TWIN FIXED WINDOWS, TEMPERED AT STAIR                 |  |
| 1W 2852 CSMT       | 2'-8" | 5'-2"  | METAL    | PRE-FINISHED | 6 LITE     | 3        | BEDROOM NO. 4, OPEN OFFICE (UPPER LEVEL), HOME GYM                   | TWIN CASEMENT WINDOWS                                 |  |
| (3) 2852 CSMT      | 2'-8" | 5'-2"  | METAL    | PRE-FINISHED | 6 LITE     | 1        | JR. MASTER BEDROOM                                                   | TRIPLE CASEMENT WINDOWS                               |  |
| (4) 2852 CSMT      | 2'-8" | 5'-2"  | METAL    | PRE-FINISHED | 6 LITE     | 3        | GARAGE A, GARAGE B                                                   | QUAD FIXED WINDOWS                                    |  |
| (3) 2852 CSMT      | 2'-8" | 6'-2"  | METAL    | PRE-FINISHED | 6 LITE     | 2        | BEDROOM NO. 5, HOME GYM                                              | TRIPLE CASEMENT WINDOWS                               |  |
| 1W 2872 FIXED      | 2'-8" | 7'-2"  | METAL    | PRE-FINISHED | 6 LITE     | 1        | OFFICE                                                               | TWIN FIXED WINDOWS, TEMPERED                          |  |
| (3) 2872 CSMT      | 2'-8" | 7'-2"  | METAL    | PRE-FINISHED | 6 LITE     | 1        | QUEST BEDROOM                                                        | TRIPLE CASEMENT WINDOWS, TEMPERED                     |  |
| (3) 2860 FIXED W/  | 2'-8" | 6'-0"  | METAL    | PRE-FINISHED | 6 LITE     | 1        | DINING ROOM                                                          | TRIPLE CASEMENT WINDOWS (TEMPERED) W/ TRIPLE TRANSOMS |  |
| (3) 2850 TRANSOM   | 2'-8" | 2'-0"  | METAL    | PRE-FINISHED | 2 LITE     | 2        | LAUNDRY                                                              | TWIN FIXED WINDOWS, TEMPERED                          |  |
| 1W 2860 FIXED      | 2'-8" | 5'-0"  | METAL    | PRE-FINISHED | 6 LITE     | 1        | LAUNDRY                                                              | TWIN FIXED WINDOWS, TEMPERED                          |  |
| (3) 3080 FIXED     | 3'-0" | 8'-0"  | METAL    | PRE-FINISHED | 6 LITE     | 2        | STAIR                                                                | TRIPLE FIXED WINDOWS, TEMPERED                        |  |
| (2) 5020 TRANSOM   | 5'-0" | 2'-0"  | METAL    | PRE-FINISHED | 3 LITE     | 1        | MASTER BATH                                                          | (2) TRANSOM WINDOWS, TEMPERED                         |  |
| 6020 TRANSOM       | 6'-0" | 2'-0"  | METAL    | PRE-FINISHED | 3 LITE     | 2        | JR. MASTER BEDROOM, BEDROOM NO. 4                                    | TRANSOM WINDOW                                        |  |
| 8020 FIXED         | 8'-0" | 10'-0" | METAL    | PRE-FINISHED | 1 LITE     | 1        | GREAT ROOM                                                           | FIXED WINDOW, TEMPERED                                |  |
| 5070 FIXED W/      | 5'-0" | 7'-0"  | METAL    | PRE-FINISHED | 1 LITE     | 2        | GREAT ROOM                                                           |                                                       |  |
| 5020 TRANSOM       | 5'-0" | 2'-0"  | METAL    | PRE-FINISHED | 1 LITE     | 2        | GREAT ROOM                                                           |                                                       |  |
| 8070 FIXED W/      | 8'-0" | 7'-0"  | METAL    | PRE-FINISHED | 1 LITE     | 1        | GREAT ROOM                                                           |                                                       |  |
| 8020 TRANSOM       | 8'-0" | 2'-0"  | METAL    | PRE-FINISHED | 1 LITE     | 1        | GREAT ROOM                                                           |                                                       |  |

NOTE: REFER TO ACTUAL WINDOW SUPPLIER'S SPECIFICATIONS FOR ALL ROUGH OPENINGS.

| EXTERIOR DOOR SCHEDULE     |    |        |        |               |              |          |                                                                      |  |  |
|----------------------------|----|--------|--------|---------------|--------------|----------|----------------------------------------------------------------------|--|--|
| DOOR DESCRIPTION           | PR | WIDTH  | HEIGHT | MATERIAL      | FINISH       | QUANTITY | REMARKS                                                              |  |  |
| PR 30100 W 30100 EACH SIDE | Y  | 3'-0"  | 10'-0" | STEEL / GLASS | PRE-FINISHED | 1        | FRONT DOOR, 6 LITE                                                   |  |  |
| 16080 GLASS FOLDING        | N  | 16'-0" | 10'-0" | METAL         | PRE-FINISHED | 1        | GLASS SLIDING DOOR                                                   |  |  |
| 12080 GLASS SLIDER         | N  | 12'-0" | 8'-0"  | METAL         | PRE-FINISHED | 4        | GLASS SLIDING DOOR AT FAMILY ROOM, MASTER BEDROOM, LOUNGE            |  |  |
| PR 26100 FRENCH            | Y  | 2'-6"  | 10'-0" | METAL         | PRE-FINISHED | 2        | FRENCH DOOR, 1 LITE                                                  |  |  |
| 2/4                        | N  | 2'-4"  | 8'-0"  | METAL         | PRE-FINISHED | 1        | POOL BATH, NO GLASS                                                  |  |  |
| 2/8 FRENCH                 | N  | 2'-4"  | 8'-0"  | METAL         | PRE-FINISHED | 1        | MUDROOM, 1 LITE                                                      |  |  |
| 3/0                        | N  | 3'-0"  | 8'-0"  | METAL         | PRE-FINISHED | 2        | POOL STORAGE, GARAGE B, NO GLASS                                     |  |  |
| 3/0                        | N  | 3'-0"  | 8'-0"  | STEEL / GLASS | PRE-FINISHED | 2        | MUDROOM ENTRY DOORS, GARAGE B, 6 LITE AT MAIN FACADE, 1 LITE AT REAR |  |  |
| PR 3/0 FRENCH              | Y  | 3'-0"  | 8'-0"  | METAL         | PRE-FINISHED | 1        | FAMILY ROOM, 6 LITE                                                  |  |  |

NOTE: REFER TO ACTUAL DOOR SUPPLIER'S SPECIFICATIONS FOR ALL ROUGH OPENINGS.

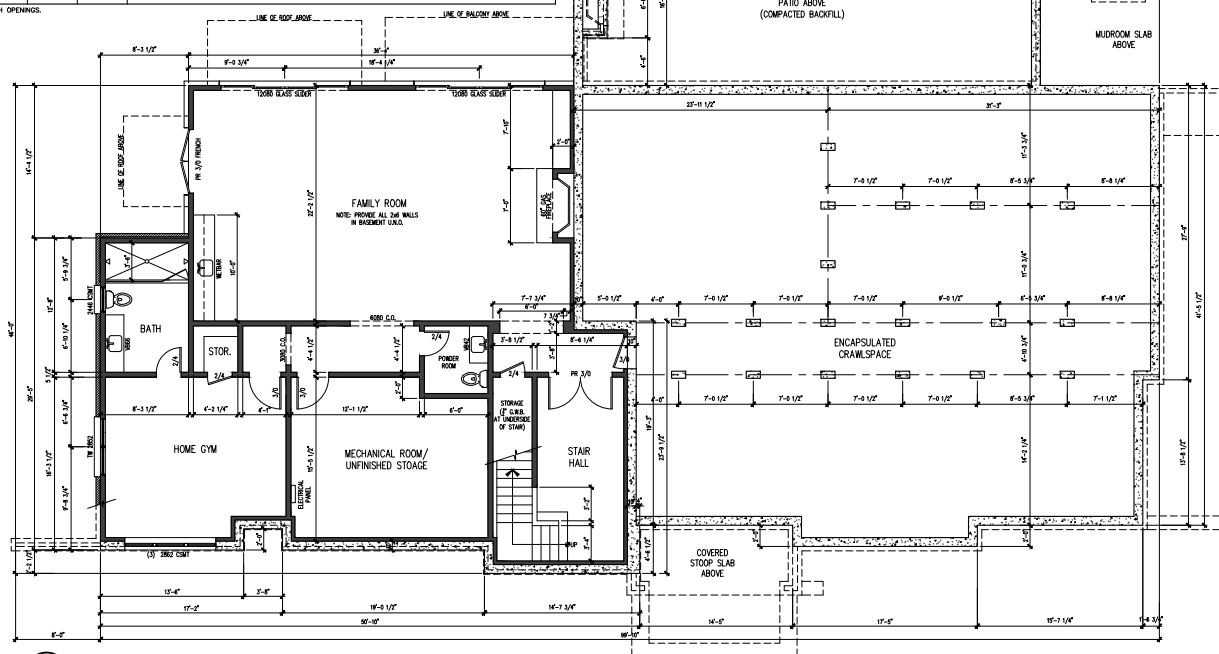

1 BASEMENT LEVEL FLOOR PLAN  
A100 3/16"=1'-0"

RELEASED FOR  
CONSTRUCTION

Drawn:  
Checked:  
Date:  
Job No.:

Revisions:

No. Date

15152 HOPEWELL ROAD  
A NEW HOUSE PROJECT  
MILTON, GEORGIA



GOODMAN DESIGN  
1000 ALPHARETTA, GEORGIA 30009  
ph (878) 427-8468  
info@goodmandesign.com  
creating architecture for sustainable environments

Consultants: Process Design with Purpose


The BASEMENT  
FLOOR  
PLAN

Scale: 3/16"=1'-0"


Sheet:

A100

of:

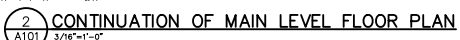

of:

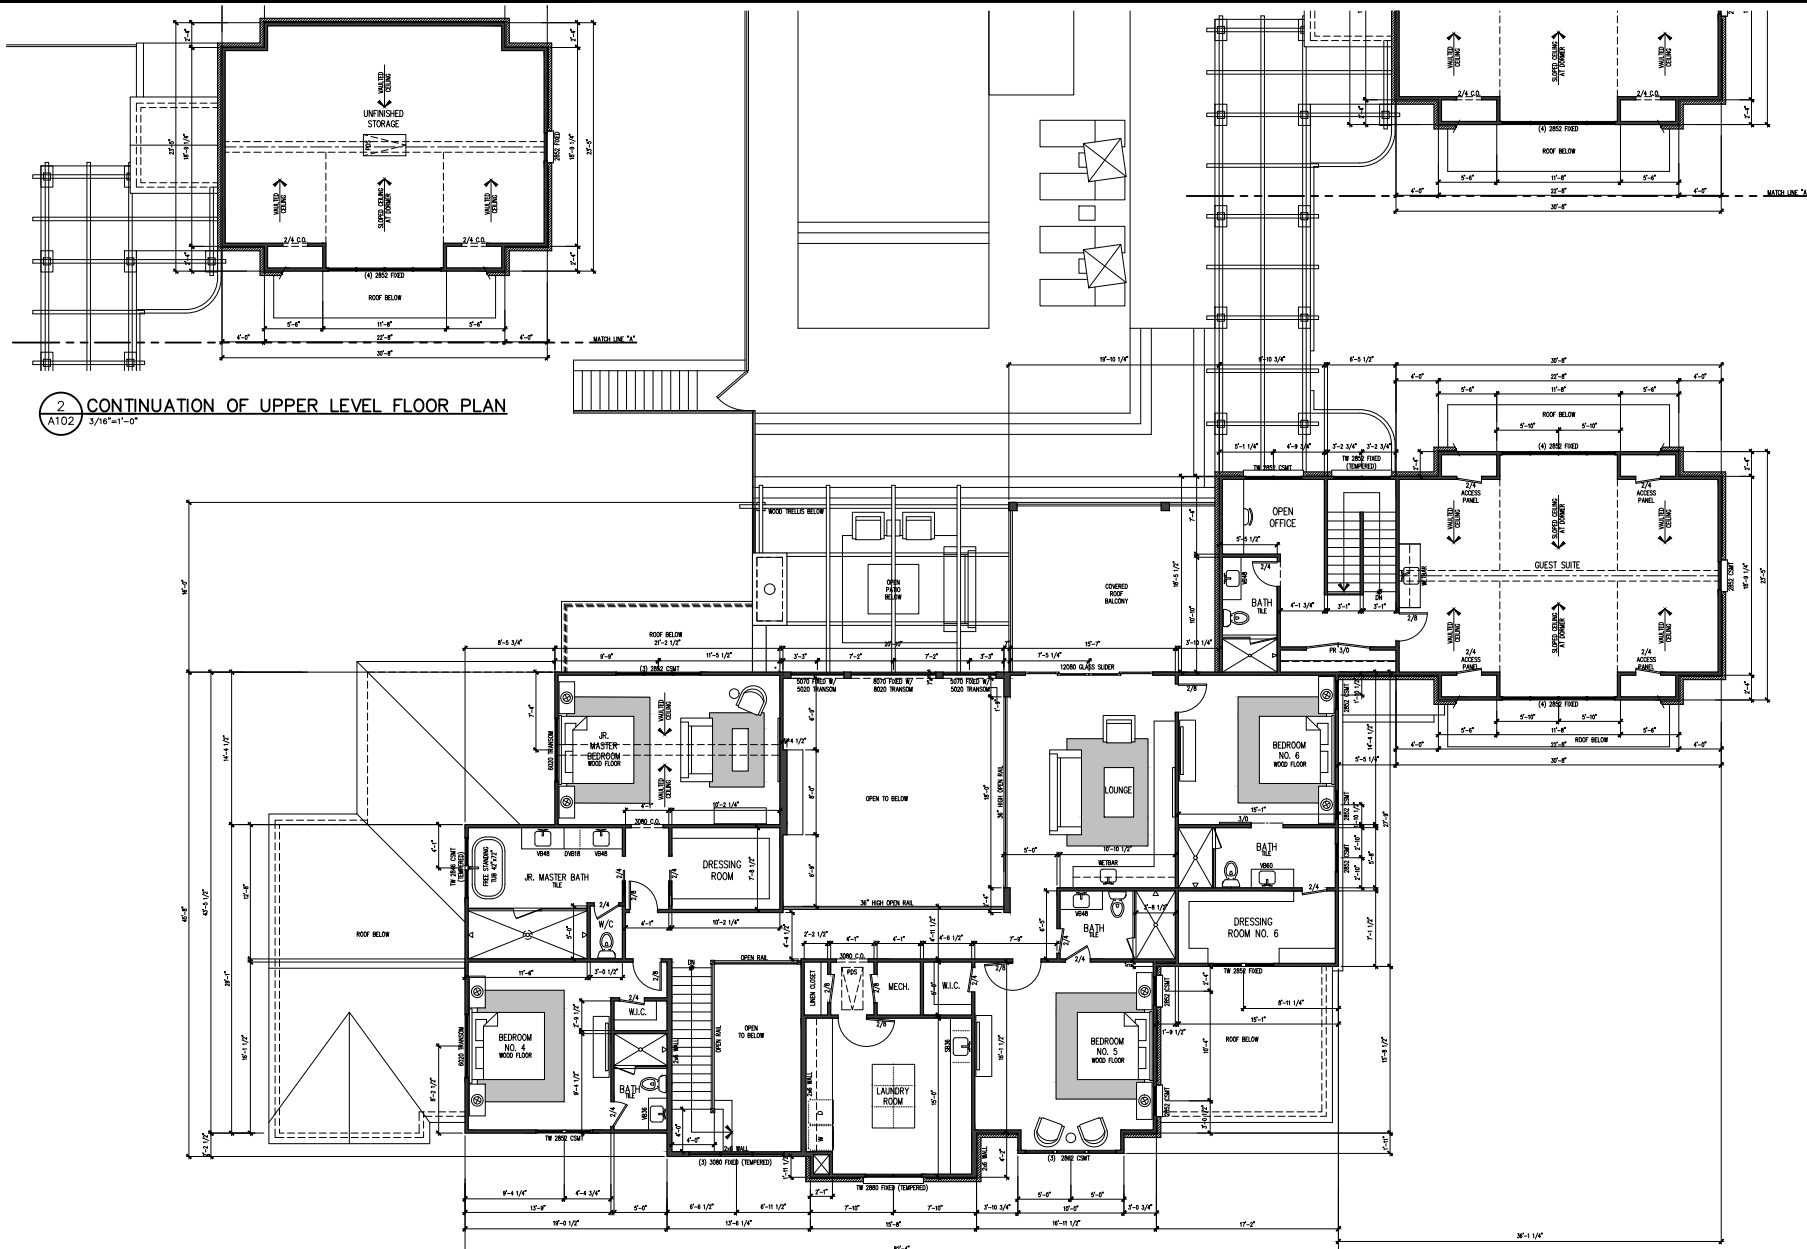

2 CONTINUATION OF UPPER LEVEL FLOOR PLAN  
3/16"=1'-0"

1 UPPER LEVEL FLOOR PLAN  
3/16"=1'-0"

RELEASED FOR  
CONSTRUCTION

|            |      |
|------------|------|
| Drawn:     |      |
| Checked:   |      |
| Date:      |      |
| Job No.:   |      |
| Revisions: |      |
| No.        | Date |

15152 HOPEWELL ROAD  
A NEW HOUSE PROJECT  
MILTON, GEORGIA



GOODMAN DESIGN  
1000 PINEHURST DRIVE  
ALPHARETTA, GEORGIA 30009  
ph (878) 427-8486  
info@goodmandesign.com  
creating architecture for sustainable environments

Process: Plans  
Credits: Design with Purpose

THE UPPER LEVEL  
FLOOR  
PLAN

Scale:  
3/16"=1'-0"

Sheet:

A102

of: